

Дом 4х3м ББ

Альбом

Дом 4х3м ББ

Альбом

2025

### Ведомость рабочих чертежей основного комплекта

| №<br>Листа | Наименование                                                     | Примечание |
|------------|------------------------------------------------------------------|------------|
| 1          | Общие данные                                                     |            |
| 2          | Вид 1                                                            |            |
| 3          | Вид 2                                                            |            |
| 4          | Вид 3                                                            |            |
| 5          | Вид 4                                                            |            |
| 6          | План балок на отм. -0,285                                        |            |
| 7          | План балок на отм. -0,035                                        |            |
| 8          | План на отм. 0,000                                               |            |
| 9          | Развертка по стене (оси) 1<br>Материал: Сосна, Минибрус 45x145мм |            |
| 10         | Развертка по стене (оси) 2<br>Материал: Сосна, Минибрус 45x145мм |            |
| 11         | Развертка по стене (оси) А<br>Материал: Сосна, Минибрус 45x145мм |            |
| 12         | Развертка по стене (оси) Б<br>Материал: Сосна, Минибрус 45x145мм |            |
| 13         | Развертка по стене (оси) В<br>Материал: Сосна, Минибрус 45x145мм |            |
| 14         | Развертка по стене (оси) Г<br>Материал: Сосна, Минибрус 45x145мм |            |
| 15         | Развертка по стене (оси) Д<br>Материал: Сосна, Минибрус 45x145мм |            |
| 16         | План кровли                                                      |            |
| 17         | Развертка ската № 6                                              |            |
| 18         | Развертка ската № 7                                              |            |
| 19         | Разрез 1 - 1                                                     |            |

|      |          |      |        |         |      |             |        |      |
|------|----------|------|--------|---------|------|-------------|--------|------|
|      |          |      |        |         |      | - АР        |        |      |
| Изм. | Кол. уч. | Лист | № док. | Подпись | Дата |             |        |      |
|      |          |      |        |         |      | Дом 4х3м ББ | Стадия | Лист |
|      |          |      |        |         |      |             |        | 1.1  |
|      |          |      |        |         |      |             |        | 2    |
|      |          |      |        |         |      |             |        |      |
|      |          |      |        |         |      |             |        |      |

Ведомость основных комплектов рабочих чертежей


| Обозначение | Наименование                      | Примечание |
|-------------|-----------------------------------|------------|
| - АР        | Архитектурные решения             |            |
| - АС        | Архитектурно-строительные решения |            |




|            |          |      |        |         |      |             |        |      |        |
|------------|----------|------|--------|---------|------|-------------|--------|------|--------|
|            |          |      |        |         |      | - АС        |        |      |        |
|            |          |      |        |         |      |             |        |      |        |
|            |          |      |        | Изм.    | Кол. |             |        |      |        |
| Изм.       | Кол. уч. | Лист | № док. | Подпись | Дата |             |        |      |        |
| Разработал |          |      |        |         |      | Дом 4х3м ББ | Стадия | Лист | Листов |
|            |          |      |        |         |      |             |        | 2    |        |
|            |          |      |        |         |      |             |        |      |        |
|            |          |      |        |         |      | Вид 1       |        |      |        |
|            |          |      |        |         |      |             |        |      |        |
|            |          |      |        |         |      |             |        |      |        |



|            |          |      |        |         |      |             |        |      |        |
|------------|----------|------|--------|---------|------|-------------|--------|------|--------|
|            |          |      |        |         |      | - АС        |        |      |        |
|            |          |      |        |         |      |             |        |      |        |
|            |          |      |        | Изм.    | Кол. |             |        |      |        |
| Изм.       | Кол. уч. | Лист | № док. | Подпись | Дата |             |        |      |        |
| Разработал |          |      |        |         |      | Дом 4х3м ББ | Стадия | Лист | Листов |
|            |          |      |        |         |      |             |        | 3    |        |
|            |          |      |        |         |      |             |        |      |        |
|            |          |      |        |         |      | Вид 2       |        |      |        |
|            |          |      |        |         |      |             |        |      |        |
|            |          |      |        |         |      |             |        |      |        |

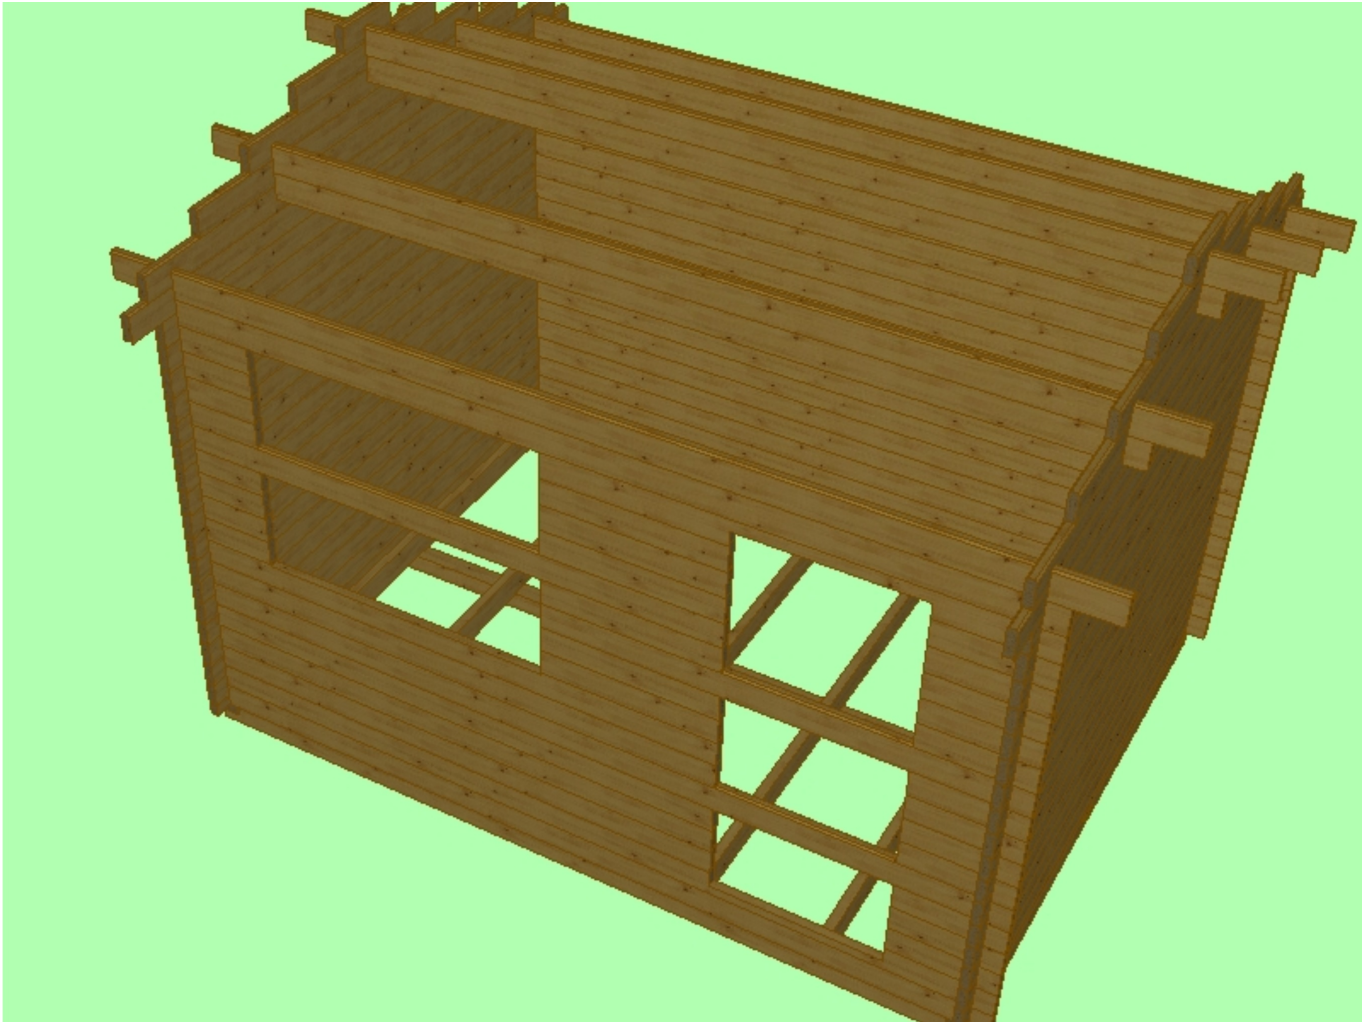


|            |          |      |        |         |      |             |        |      |        |
|------------|----------|------|--------|---------|------|-------------|--------|------|--------|
|            |          |      |        |         |      | - АС        |        |      |        |
|            |          |      |        |         |      |             |        |      |        |
|            |          |      |        | Изм.    | Кол. |             |        |      |        |
| Изм.       | Кол. уч. | Лист | № док. | Подпись | Дата |             |        |      |        |
| Разработал |          |      |        |         |      | Дом 4х3м ББ | Стадия | Лист | Листов |
|            |          |      |        |         |      |             |        | 4    |        |
|            |          |      |        |         |      |             |        |      |        |
|            |          |      |        |         |      | Вид 3       |        |      |        |
|            |          |      |        |         |      |             |        |      |        |
|            |          |      |        |         |      |             |        |      |        |

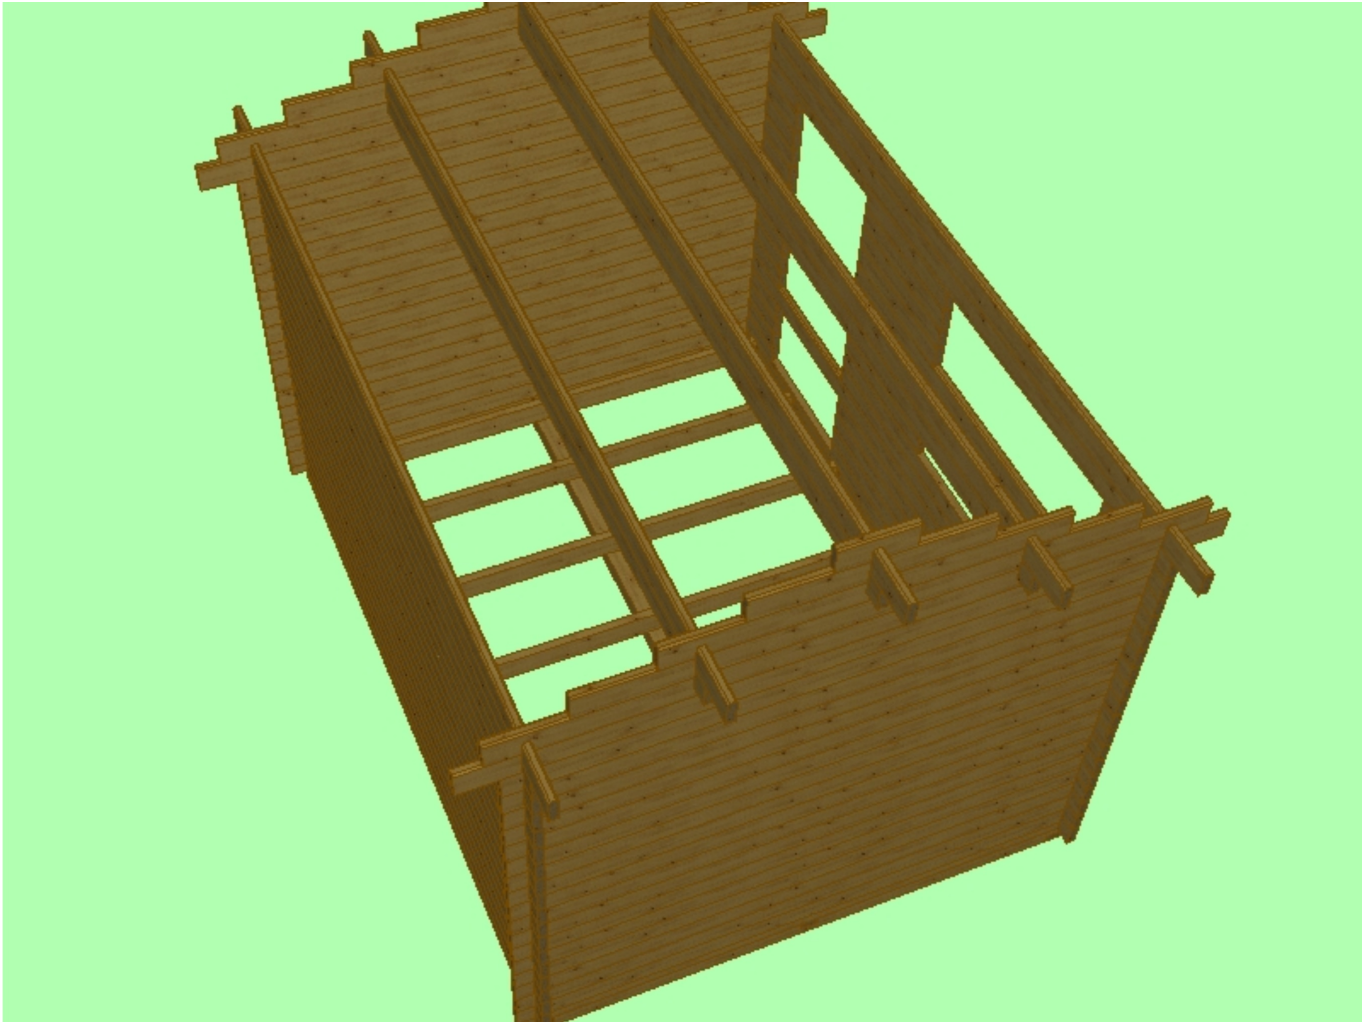


|            |          |      |        |         |      |             |        |      |        |
|------------|----------|------|--------|---------|------|-------------|--------|------|--------|
|            |          |      |        |         |      | - АС        |        |      |        |
|            |          |      |        |         |      |             |        |      |        |
|            |          |      |        | Изм.    | Кол. |             |        |      |        |
| Изм.       | Кол. уч. | Лист | № док. | Подпись | Дата |             |        |      |        |
| Разработал |          |      |        |         |      | Дом 4х3м ББ | Стадия | Лист | Листов |
|            |          |      |        |         |      |             |        | 5    |        |
|            |          |      |        |         |      |             |        |      |        |
|            |          |      |        |         |      | Вид 4       |        |      |        |
|            |          |      |        |         |      |             |        |      |        |
|            |          |      |        |         |      |             |        |      |        |




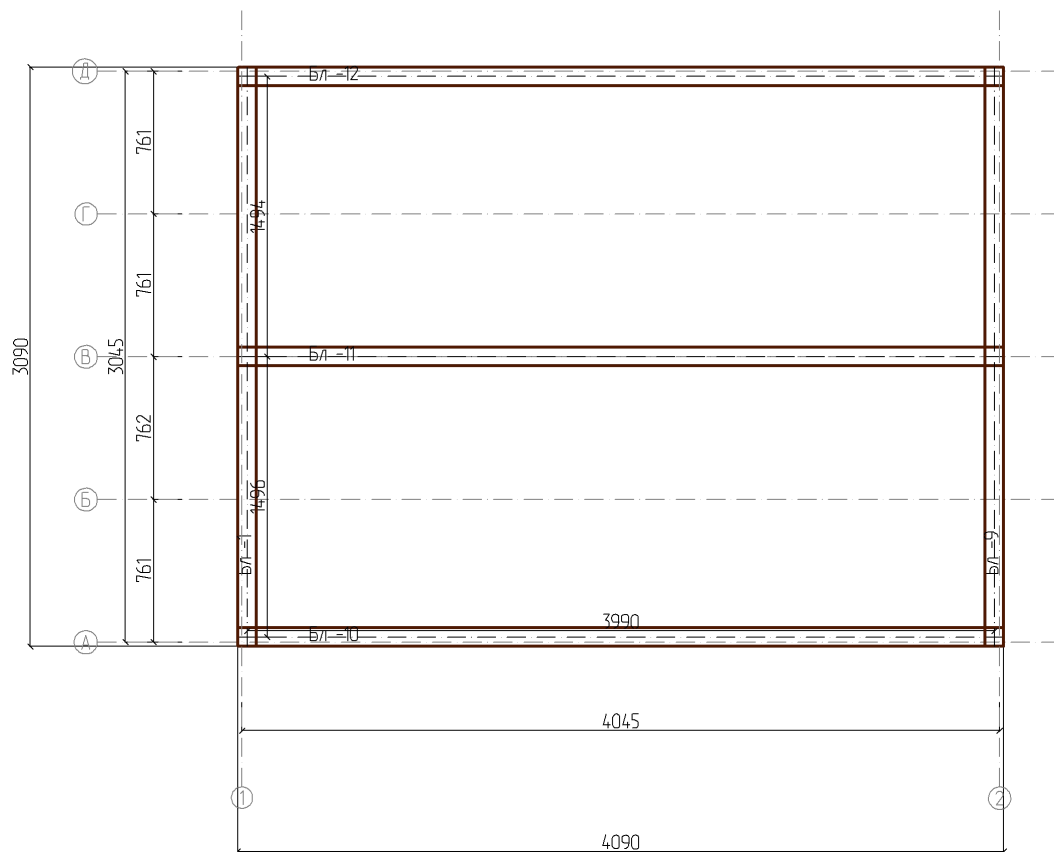


|            |          |      |        |         |      |                                       |        |      |        |
|------------|----------|------|--------|---------|------|---------------------------------------|--------|------|--------|
|            |          |      |        |         |      | - АР                                  |        |      |        |
|            |          |      |        |         |      |                                       |        |      |        |
|            |          |      |        | Изм.    | Кол. |                                       |        |      |        |
| Изм.       | Кол. уч. | Лист | № док. | Подпись | Дата |                                       |        |      |        |
| Разработал |          |      |        |         |      | Дом 4х3м ББ                           | Стадия | Лист | Листов |
|            |          |      |        |         |      |                                       |        | 6    |        |
|            |          |      |        |         |      |                                       |        |      |        |
|            |          |      |        |         |      | План балок на отм. -0,285<br>М 1 : 40 |        |      |        |
|            |          |      |        |         |      |                                       |        |      |        |
|            |          |      |        |         |      |                                       |        |      |        |

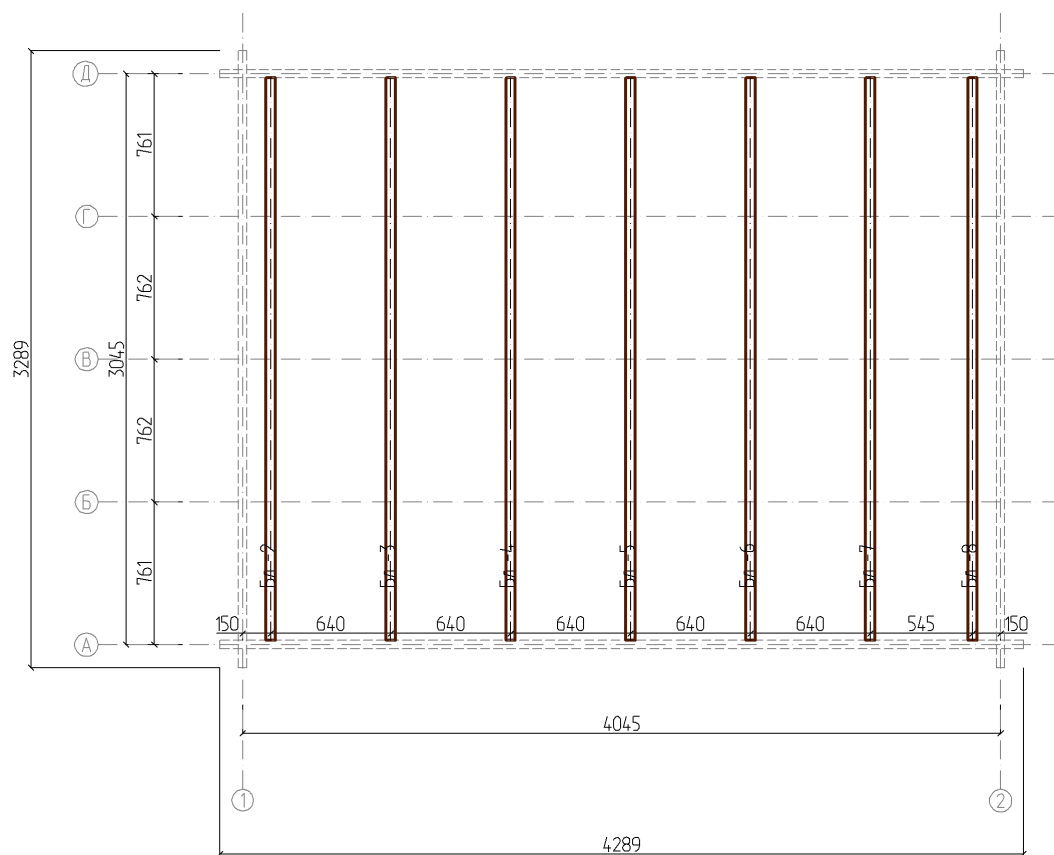


|            |          |      |        |         |      |                                       |        |      |        |
|------------|----------|------|--------|---------|------|---------------------------------------|--------|------|--------|
|            |          |      |        |         |      | - АР                                  |        |      |        |
|            |          |      |        |         |      |                                       |        |      |        |
|            |          |      |        | Изм.    | Кол. |                                       |        |      |        |
| Изм.       | Кол. уч. | Лист | № док. | Подпись | Дата |                                       |        |      |        |
| Разработал |          |      |        |         |      | Дом 4х3м ББ                           | Стадия | Лист | Листов |
|            |          |      |        |         |      |                                       |        | 7    |        |
|            |          |      |        |         |      |                                       |        |      |        |
|            |          |      |        |         |      | План балок на отм. -0,035<br>М 1 : 40 |        |      |        |
|            |          |      |        |         |      |                                       |        |      |        |

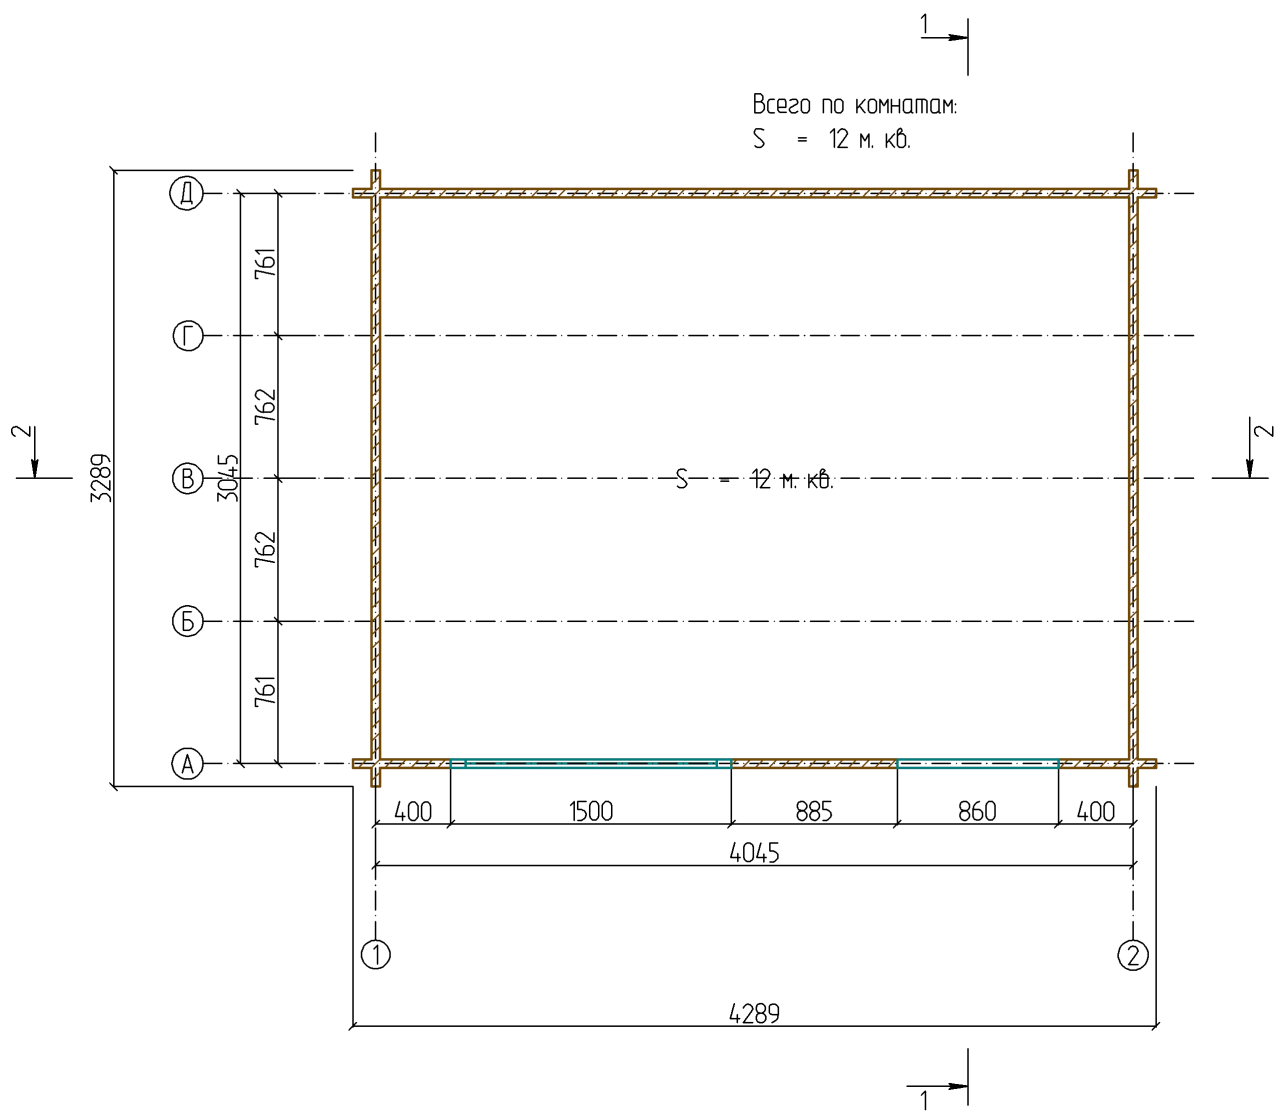


|            |          |      |        |         |      |                                |        |      |        |
|------------|----------|------|--------|---------|------|--------------------------------|--------|------|--------|
|            |          |      |        |         |      | - АР                           |        |      |        |
|            |          |      |        |         |      |                                |        |      |        |
|            |          |      |        | Изм.    | Кол. |                                |        |      |        |
| Изм.       | Кол. уч. | Лист | № док. | Подпись | Дата |                                |        |      |        |
| Разработал |          |      |        |         |      | Дом 4х3м ББ                    | Стадия | Лист | Листов |
|            |          |      |        |         |      |                                |        | 8    |        |
|            |          |      |        |         |      |                                |        |      |        |
|            |          |      |        |         |      | План на отм. 0,000<br>М 1 : 40 |        |      |        |
|            |          |      |        |         |      |                                |        |      |        |
|            |          |      |        |         |      |                                |        |      |        |

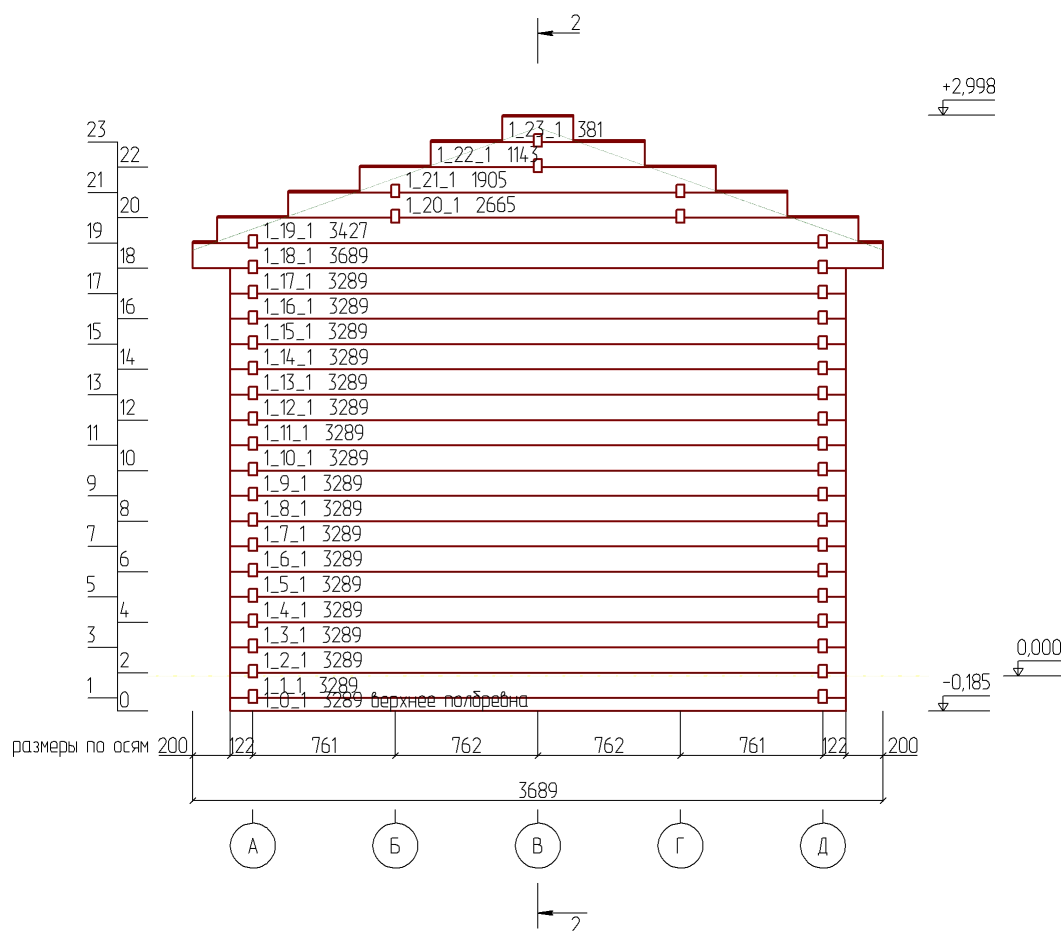


|            |          |      |        |         |      |                                                                              |        |      |        |
|------------|----------|------|--------|---------|------|------------------------------------------------------------------------------|--------|------|--------|
|            |          |      |        |         |      | - АС                                                                         |        |      |        |
|            |          |      |        |         |      |                                                                              |        |      |        |
|            |          |      |        |         |      |                                                                              |        |      |        |
|            |          |      |        | Изм.    | Кол. |                                                                              |        |      |        |
| Изм.       | Кол. уч. | Лист | № док. | Подпись | Дата |                                                                              |        |      |        |
| Разработал |          |      |        |         |      | Дом 4х3м ББ                                                                  | Стадия | Лист | Листов |
|            |          |      |        |         |      |                                                                              |        | 9    |        |
|            |          |      |        |         |      |                                                                              |        |      |        |
|            |          |      |        |         |      |                                                                              |        |      |        |
|            |          |      |        |         |      | Развертка по стене (оси) 1<br>Материал: Сосна, Минибрус 45х145мм<br>М 1 : 40 |        |      |        |
|            |          |      |        |         |      |                                                                              |        |      |        |
|            |          |      |        |         |      |                                                                              |        |      |        |

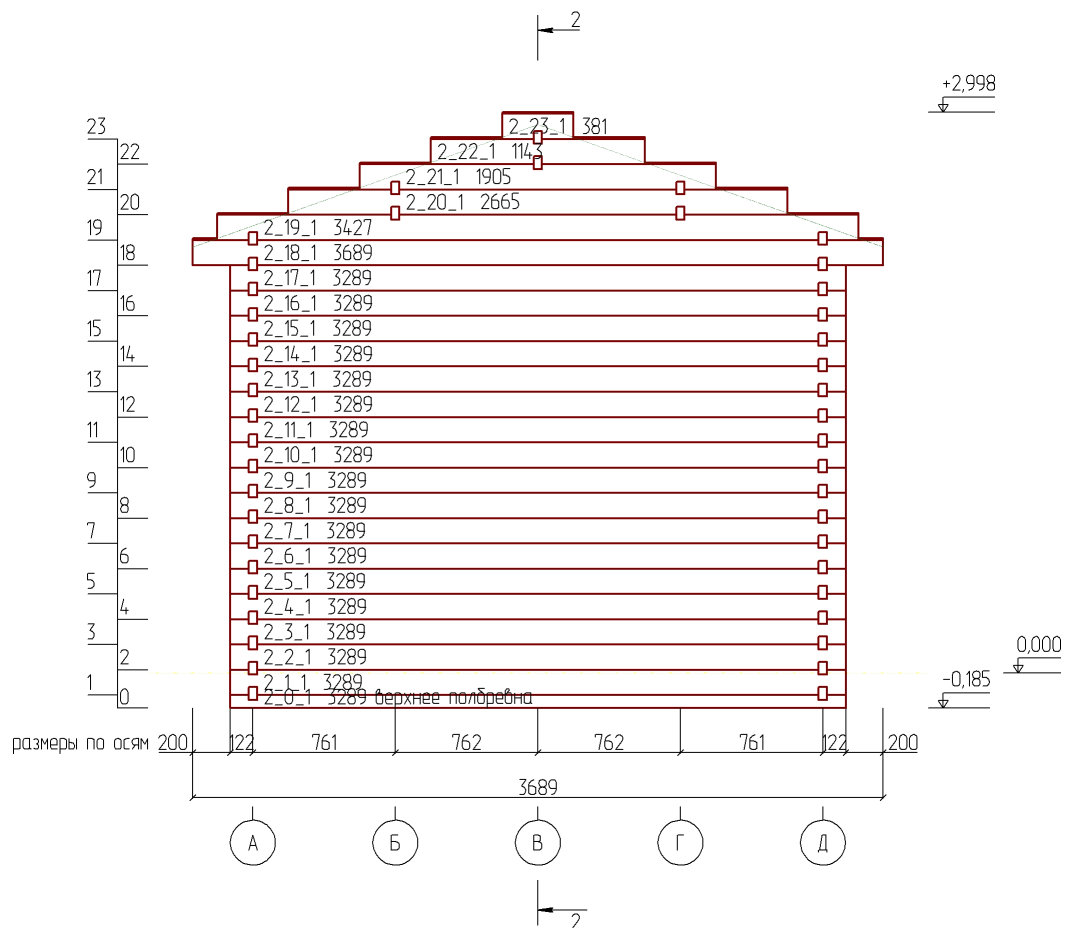


|            |          |      |        |         |      |                                                                              |        |      |        |
|------------|----------|------|--------|---------|------|------------------------------------------------------------------------------|--------|------|--------|
|            |          |      |        |         |      | - АС                                                                         |        |      |        |
|            |          |      |        |         |      |                                                                              |        |      |        |
|            |          |      |        |         |      |                                                                              |        |      |        |
|            |          |      |        | Изм.    | Кол. |                                                                              |        |      |        |
| Изм.       | Кол. уч. | Лист | № док. | Подпись | Дата |                                                                              |        |      |        |
| Разработал |          |      |        |         |      | Дом 4х3м ББ                                                                  | Стадия | Лист | Листов |
|            |          |      |        |         |      |                                                                              |        | 10   |        |
|            |          |      |        |         |      |                                                                              |        |      |        |
|            |          |      |        |         |      |                                                                              |        |      |        |
|            |          |      |        |         |      | Развертка по стене (оси) 2<br>Материал: Сосна, Минибрус 45х145мм<br>М 1 : 40 |        |      |        |
|            |          |      |        |         |      |                                                                              |        |      |        |
|            |          |      |        |         |      |                                                                              |        |      |        |

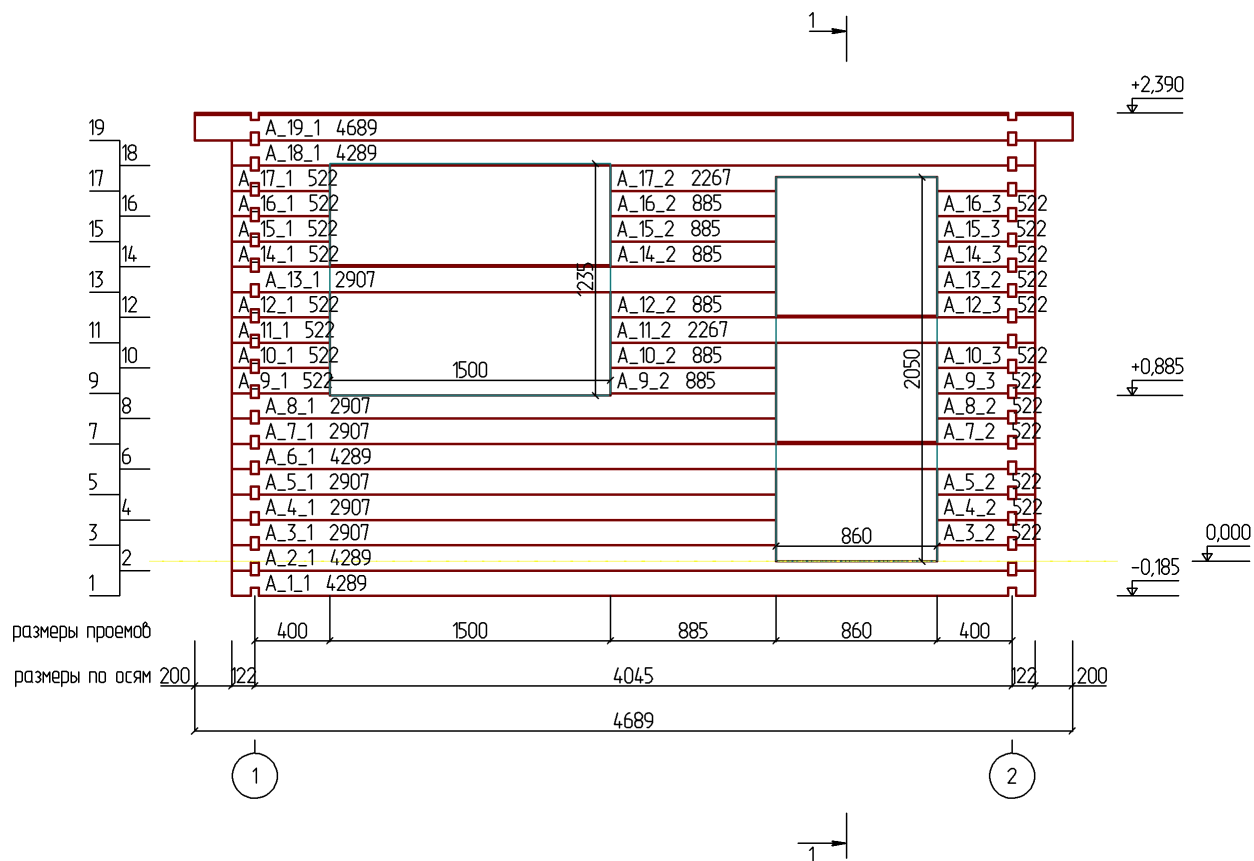

|            |          |      |        |         |      |                                    |        |      |        |
|------------|----------|------|--------|---------|------|------------------------------------|--------|------|--------|
|            |          |      |        |         |      | - АС                               |        |      |        |
|            |          |      |        |         |      |                                    |        |      |        |
|            |          |      |        | Изм.    | Кол. |                                    |        |      |        |
| Изм.       | Кол. уч. | Лист | № док. | Подпись | Дата |                                    |        |      |        |
| Разработал |          |      |        |         |      | Дом 4х3м ББ                        | Стадия | Лист | Листов |
|            |          |      |        |         |      |                                    |        | 11   |        |
|            |          |      |        |         |      |                                    |        |      |        |
|            |          |      |        |         |      | Развертка по стене (оси) А         |        |      |        |
|            |          |      |        |         |      | Материал: Сосна, Минибрус 45х145мм |        |      |        |
|            |          |      |        |         |      | М 1 : 40                           |        |      |        |

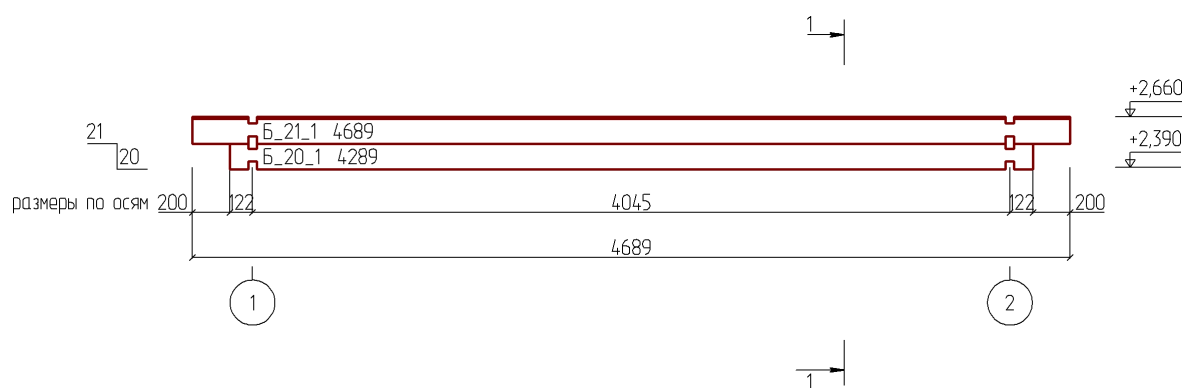


|            |          |      |        |         |      |                                                                              |        |      |        |
|------------|----------|------|--------|---------|------|------------------------------------------------------------------------------|--------|------|--------|
|            |          |      |        |         |      | - АС                                                                         |        |      |        |
|            |          |      |        |         |      |                                                                              |        |      |        |
|            |          |      |        | Изм.    | Кол. |                                                                              |        |      |        |
| Изм.       | Кол. уч. | Лист | № док. | Подпись | Дата |                                                                              |        |      |        |
| Разработал |          |      |        |         |      | Дом 4х3м ББ                                                                  | Стадия | Лист | Листов |
|            |          |      |        |         |      |                                                                              |        | 12   |        |
|            |          |      |        |         |      |                                                                              |        |      |        |
|            |          |      |        |         |      | Развертка по стене (оси) Б<br>Материал: Сосна, Минибрус 45х145мм<br>М 1 : 40 |        |      |        |
|            |          |      |        |         |      |                                                                              |        |      |        |
|            |          |      |        |         |      |                                                                              |        |      |        |

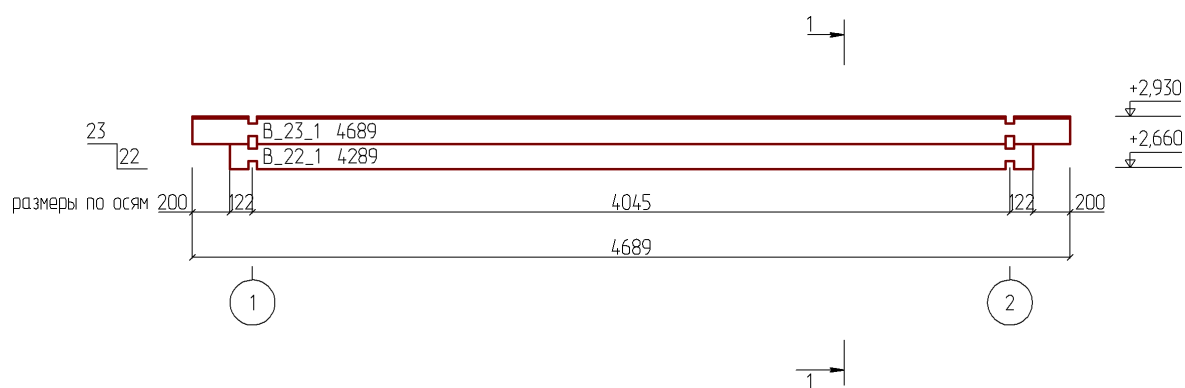


|            |          |      |        |         |      |                                                                              |        |      |        |
|------------|----------|------|--------|---------|------|------------------------------------------------------------------------------|--------|------|--------|
|            |          |      |        |         |      | - AC                                                                         |        |      |        |
|            |          |      |        |         |      |                                                                              |        |      |        |
|            |          |      |        | Изм.    | Кол. |                                                                              |        |      |        |
| Изм.       | Кол. уч. | Лист | № док. | Подпись | Дата |                                                                              |        |      |        |
| Разработал |          |      |        |         |      | Дом 4х3м ББ                                                                  | Стадия | Лист | Листов |
|            |          |      |        |         |      |                                                                              |        | 13   |        |
|            |          |      |        |         |      |                                                                              |        |      |        |
|            |          |      |        |         |      | Развертка по стене (оси) В<br>Материал: Сосна, Минибрус 45х145мм<br>М 1 : 40 |        |      |        |
|            |          |      |        |         |      |                                                                              |        |      |        |
|            |          |      |        |         |      |                                                                              |        |      |        |




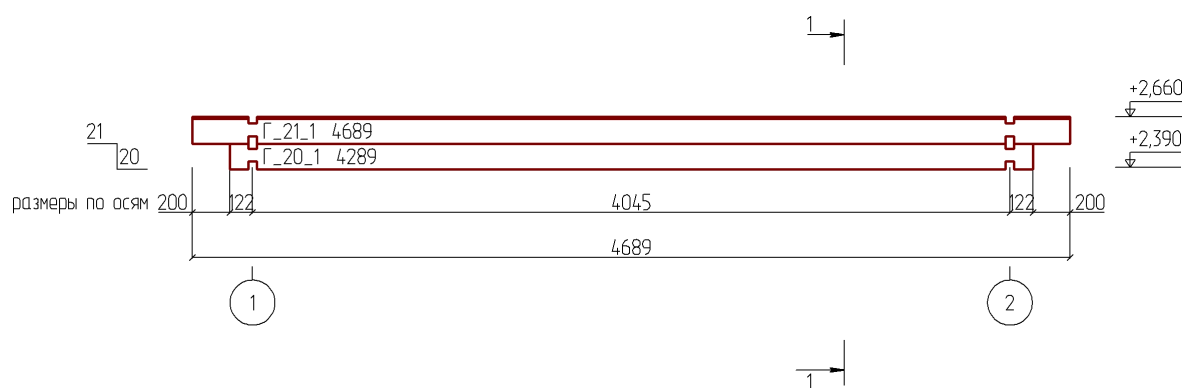


|            |          |      |        |         |      |                                                                              |        |      |        |
|------------|----------|------|--------|---------|------|------------------------------------------------------------------------------|--------|------|--------|
|            |          |      |        |         |      | - АС                                                                         |        |      |        |
|            |          |      |        |         |      |                                                                              |        |      |        |
|            |          |      |        | Изм.    | Кол. |                                                                              |        |      |        |
| Изм.       | Кол. уч. | Лист | № док. | Подпись | Дата |                                                                              |        |      |        |
| Разработал |          |      |        |         |      | Дом 4х3м ББ                                                                  | Стадия | Лист | Листов |
|            |          |      |        |         |      |                                                                              |        | 14   |        |
|            |          |      |        |         |      |                                                                              |        |      |        |
|            |          |      |        |         |      | Развертка по стене (оси) Г<br>Материал: Сосна, Минибрус 45х145мм<br>М 1 : 40 |        |      |        |
|            |          |      |        |         |      |                                                                              |        |      |        |
|            |          |      |        |         |      |                                                                              |        |      |        |

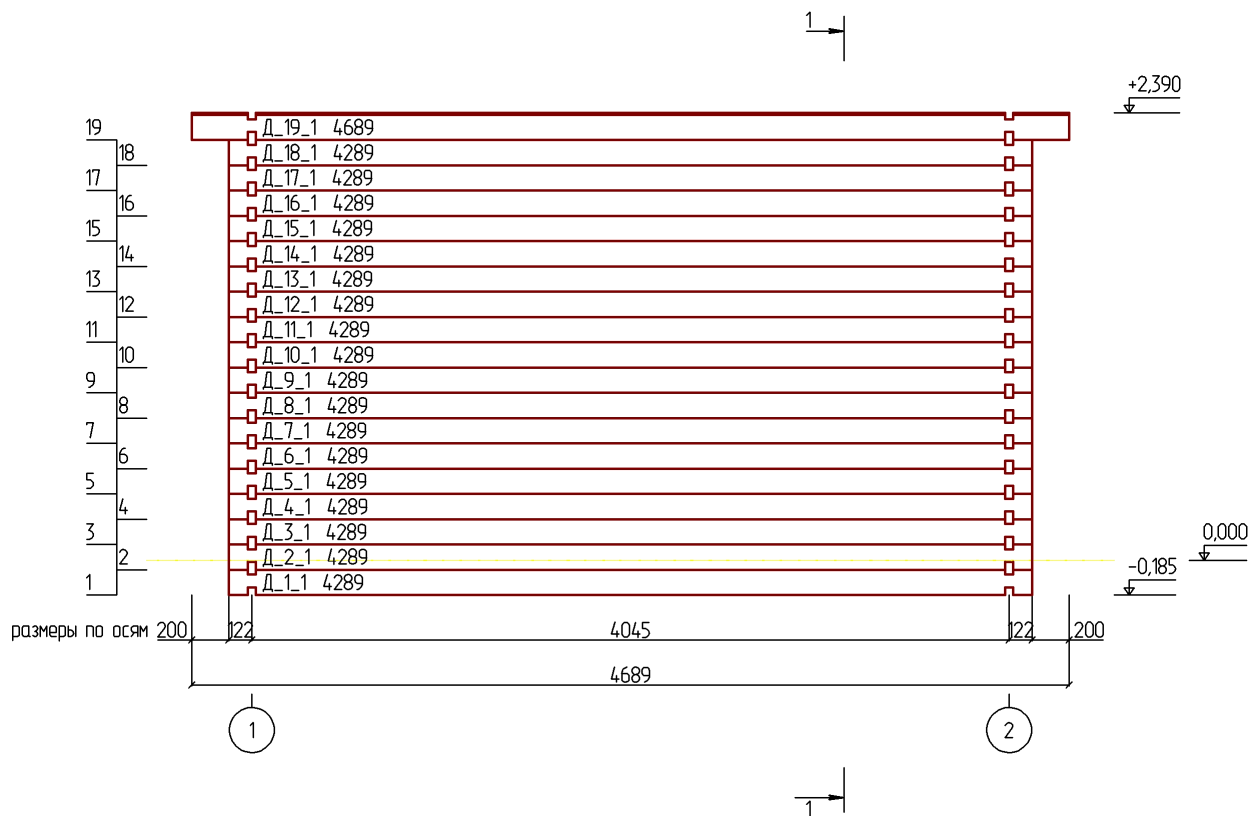

|            |          |      |        |         |      |                                    |        |      |        |
|------------|----------|------|--------|---------|------|------------------------------------|--------|------|--------|
|            |          |      |        |         |      | - АС                               |        |      |        |
|            |          |      |        |         |      |                                    |        |      |        |
|            |          |      |        | Изм.    | Кол. |                                    |        |      |        |
| Изм.       | Кол. уч. | Лист | № док. | Подпись | Дата |                                    |        |      |        |
| Разработал |          |      |        |         |      | Дом 4х3м ББ                        | Стадия | Лист | Листов |
|            |          |      |        |         |      |                                    |        | 15   |        |
|            |          |      |        |         |      |                                    |        |      |        |
|            |          |      |        |         |      | Развертка по стене (оси) Д         |        |      |        |
|            |          |      |        |         |      | Материал: Сосна, Минибрус 45х145мм |        |      |        |
|            |          |      |        |         |      | М 1 : 40                           |        |      |        |

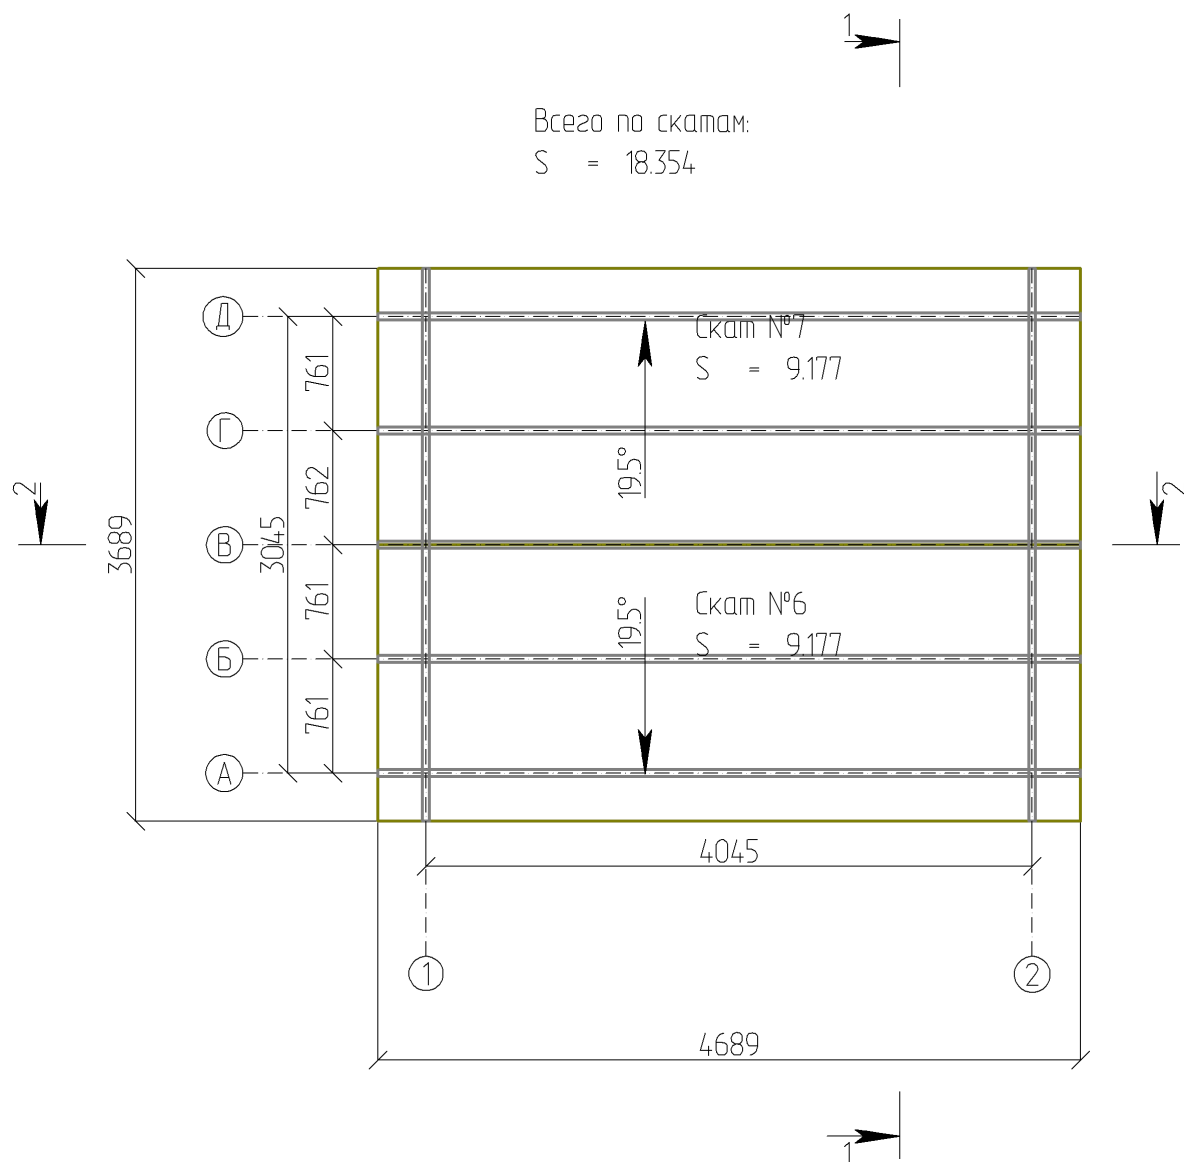


|            |          |      |        |         |      |                         |        |      |        |
|------------|----------|------|--------|---------|------|-------------------------|--------|------|--------|
|            |          |      |        |         |      | - АР                    |        |      |        |
|            |          |      |        |         |      |                         |        |      |        |
|            |          |      |        | Изм.    | Кол. |                         |        |      |        |
| Изм.       | Кол. уч. | Лист | № док. | Подпись | Дата |                         |        |      |        |
| Разработал |          |      |        |         |      | Дом 4х3м ББ             | Стадия | Лист | Листов |
|            |          |      |        |         |      |                         |        | 16   |        |
|            |          |      |        |         |      |                         |        |      |        |
|            |          |      |        |         |      | План кровли<br>М 1 : 50 |        |      |        |
|            |          |      |        |         |      |                         |        |      |        |
|            |          |      |        |         |      |                         |        |      |        |

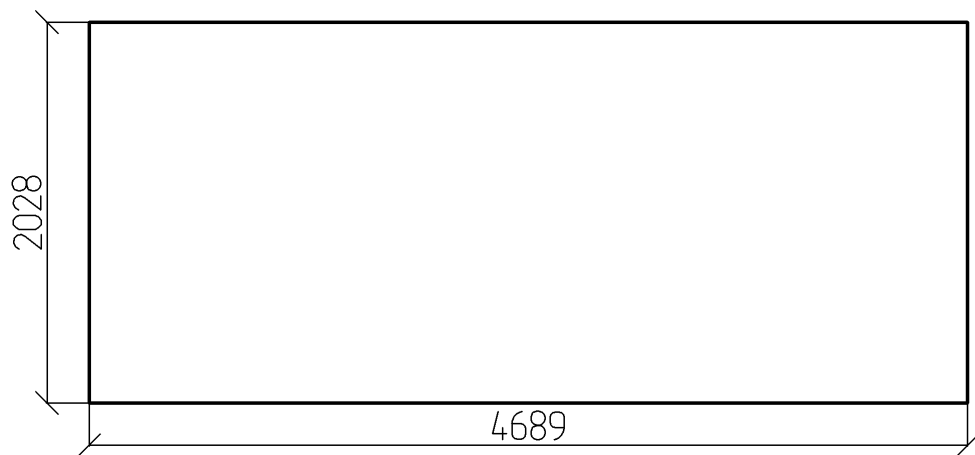

S = 9.509  
P = 13.434


|            |          |      |        |         |      |                                 |        |      |        |
|------------|----------|------|--------|---------|------|---------------------------------|--------|------|--------|
|            |          |      |        |         |      | - AC                            |        |      |        |
|            |          |      |        |         |      |                                 |        |      |        |
|            |          |      |        | Изм.    | Кол. |                                 |        |      |        |
| Изм.       | Кол. уч. | Лист | № док. | Подпись | Дата |                                 |        |      |        |
| Разработал |          |      |        |         |      | Дом 4х3м ББ                     | Стадия | Лист | Листов |
|            |          |      |        |         |      |                                 |        | 17   |        |
|            |          |      |        |         |      |                                 |        |      |        |
|            |          |      |        |         |      | Развертка ската № 6<br>М 1 : 40 |        |      |        |
|            |          |      |        |         |      |                                 |        |      |        |

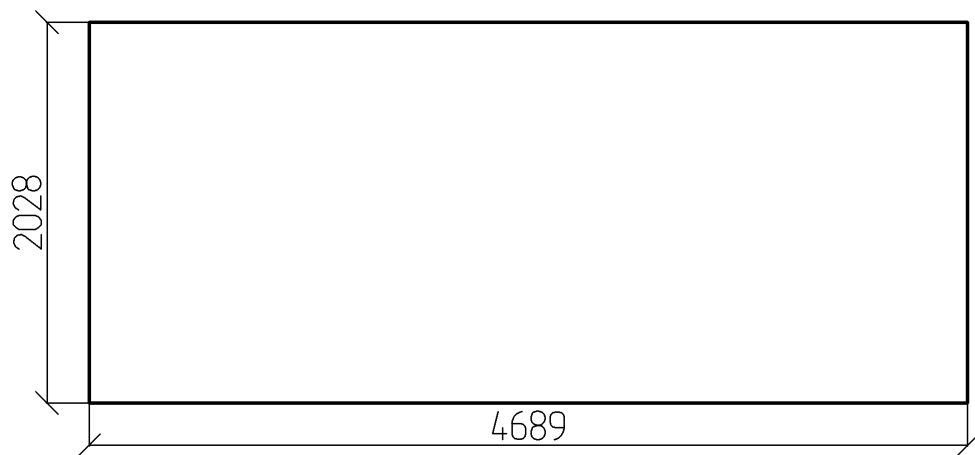

S = 9.509  
P = 13.434

|            |          |      |        |         |      |                                 |        |      |        |
|------------|----------|------|--------|---------|------|---------------------------------|--------|------|--------|
|            |          |      |        |         |      | - AC                            |        |      |        |
|            |          |      |        |         |      |                                 |        |      |        |
|            |          |      |        |         |      |                                 |        |      |        |
|            |          |      |        | Изм.    | Кол. |                                 |        |      |        |
| Изм.       | Кол. уч. | Лист | № док. | Подпись | Дата |                                 |        |      |        |
| Разработал |          |      |        |         |      | Дом 4х3м ББ                     | Стадия | Лист | Листов |
|            |          |      |        |         |      |                                 |        | 18   |        |
|            |          |      |        |         |      |                                 |        |      |        |
|            |          |      |        |         |      | Развертка ската № 7<br>М 1 : 40 |        |      |        |
|            |          |      |        |         |      |                                 |        |      |        |
|            |          |      |        |         |      |                                 |        |      |        |

# Разрез 1 - 1

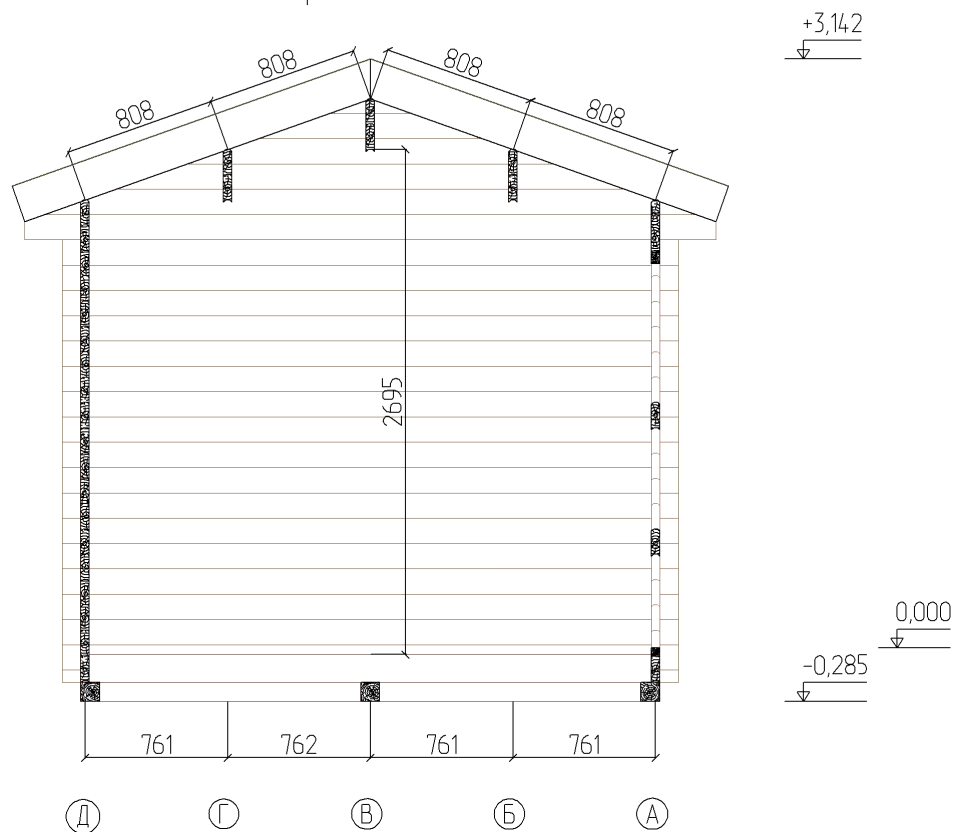

|            |          |      |        |         |      |                          |        |      |        |
|------------|----------|------|--------|---------|------|--------------------------|--------|------|--------|
|            |          |      |        |         |      | - АС                     |        |      |        |
|            |          |      |        |         |      |                          |        |      |        |
|            |          |      |        | Изм.    | Кол. |                          |        |      |        |
| Изм.       | Кол. уч. | Лист | № док. | Подпись | Дата |                          |        |      |        |
| Разработал |          |      |        |         |      | Дом 4х3м ББ              | Стадия | Лист | Листов |
|            |          |      |        |         |      |                          |        | 19   |        |
|            |          |      |        |         |      |                          |        |      |        |
|            |          |      |        |         |      | Разрез 1 - 1<br>М 1 : 40 |        |      |        |
|            |          |      |        |         |      |                          |        |      |        |
|            |          |      |        |         |      |                          |        |      |        |